Version 1.0 2018-06-20

HYBRIT AB

Denna ritning är HYBRIT:s egendom och får icke delgivas tredje man, kopieras, mångfaldigas eller på annat sätt utnyttjas utan bolagets medgivande.

HYBRITA3_A4BL2.DWG

# APPARATSPECIFIKATION

## LI355

| | |
|---|---|
| FABRIKAT | : ENDRESS & HAUSER |
| TYP | : FMR51 |
| INSIGNAL | : - |
| UTSIGNAL | : 4-20mA |
| MÄTOMR. | : 0-1200mm |
| ÖVR. DATA | : Ex ic, SIL 2 |

## -U1

| | |
|---|---|
| FABRIKAT | : ENDRESS & HAUSER |
| TYP | : RB223-B1B |
| INSIGNAL | : 4-20mA |
| UTSIGNAL | : 4-20mA |
| MÄTOMR. | : - |
| ÖVR. DATA | : - |

## -P1

| | |
|---|---|
| FABRIKAT | : ENDRESS & HAUSER |
| TYP | : FHX50 |
| INSIGNAL | : |
| UTSIGNAL | : |
| MÄTOMR. | : |
| ÖVR. DATA | : Ex ic |

| | |
|---|---|
| FABRIKAT | : |
| TYP | : |
| INSIGNAL | : |
| UTSIGNAL | : |
| MÄTOMR. | : |
| ÖVR. DATA | : |

| | |
|---|---|
| FABRIKAT | : |
| TYP | : |
| INSIGNAL | : |
| UTSIGNAL | : |
| MÄTOMR. | : |
| ÖVR. DATA | : |

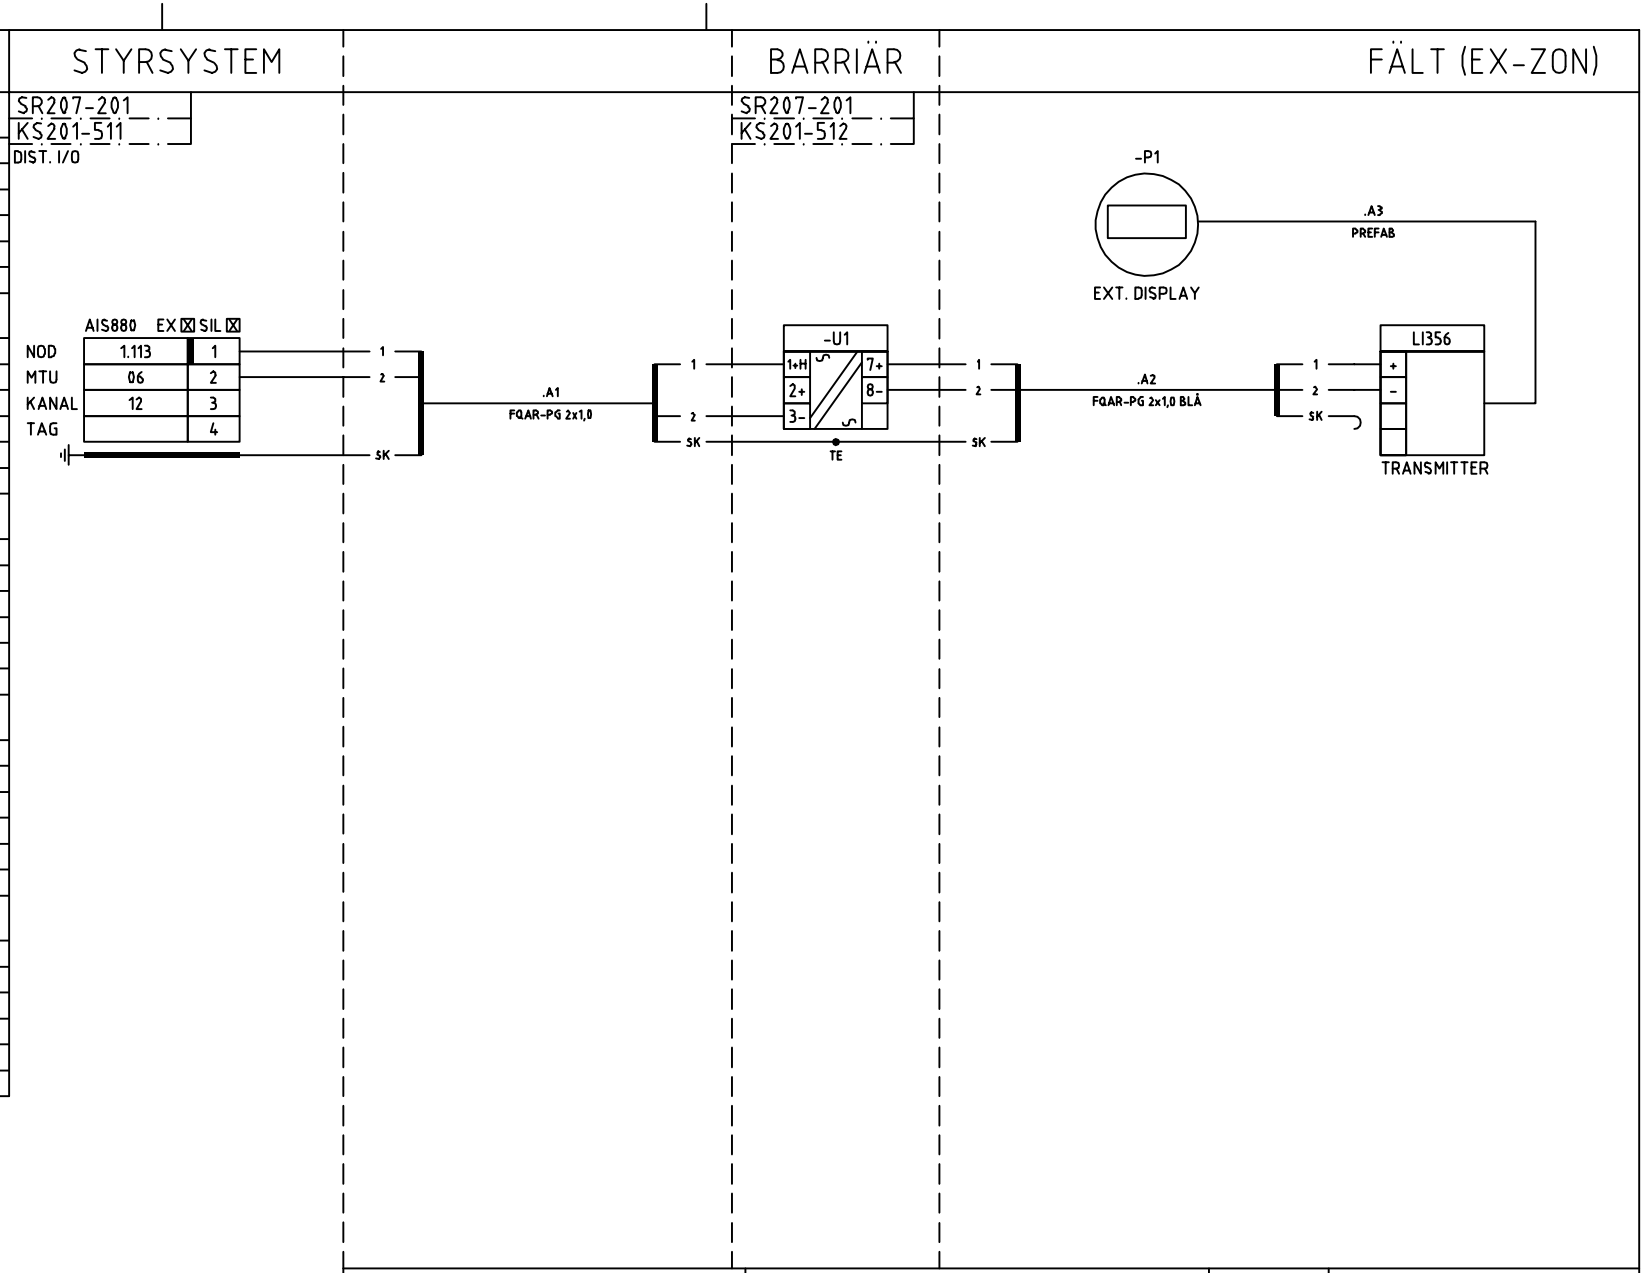


| Rev | Ändring | Datum | Inf av | Godk | Företag |
|---|---|---|---|---|---|
| 1 | Nytt I/O-nummer | 2020-03-26 | ARA | | |

| | | | |
|---|---|---|---|
| Anl. PILOTANLÄGGNING DRI | Text NIVÅMÄTNING WESP | Orig. format A4 | Dok. status ARBETSHANDLING |
| Avdeln. GASRENING TOPPGAS | HYBRIT FOSSIL-FREE STEEL | Process/ Anl. 345LI356 | Anl.del |
| Leverantör ÅF-POYRY AB | HYBRIT referens | Ritn. nr 345LI356-0001-EA | Rev 01 |