
SR207-201
KS201-511
DIST. I/O

FÄLT (EX-ZON)

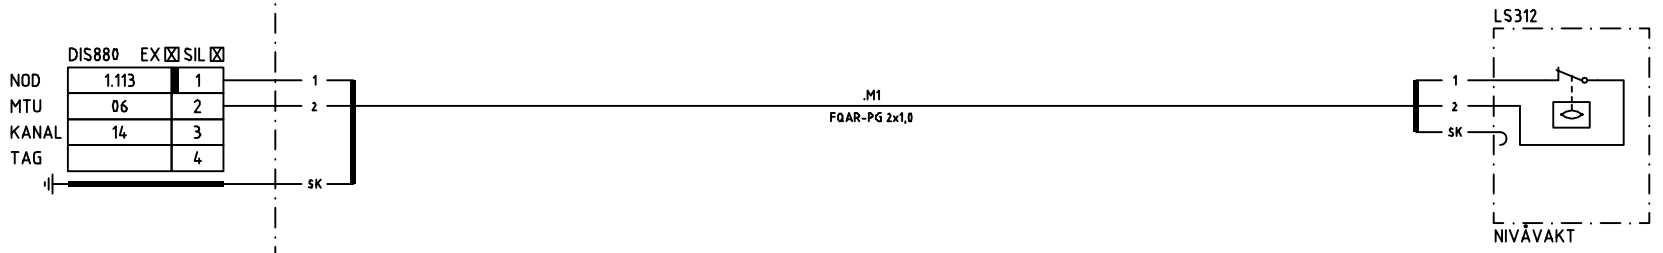

Apparat nr.	Antal	Fabrikat	Typ, Benämning, Data etc
LS312	1	Endress & Hauser	FTL51, SWITCH, Ex nA, SIL 2

Rev	Ändring	Datum	Inf av	Godk	Företag
1	Nytt I/O-nummer	2020-03-26	ARA		

Anl. PILOTANLÄGGNING DRI
Avdeln. GASRENING TOPPGAS
Leverantör ÅF-PÖYRY AB

Text NIVÅVAKT SLAMTANK
Process/ Anl. 345LS312
HYBRIT referens
Ritn. nr 345LS312-0001-EA

Orig. format A4
Dok. status ARBETSHANDLING
Anl.del
Rev 01

HYBRIT FOSSIL-FREE STEEL

Version 1.8 2018-06-28
HYBRIT AB
Denna ritning är HYBRIT:s egendom och får icke delgivas tredje man, kopieras, mångfaldigas eller på annat sätt utnyttjas utan bolagets medgivande.
HYBRITA3_A4BL2.DWG